
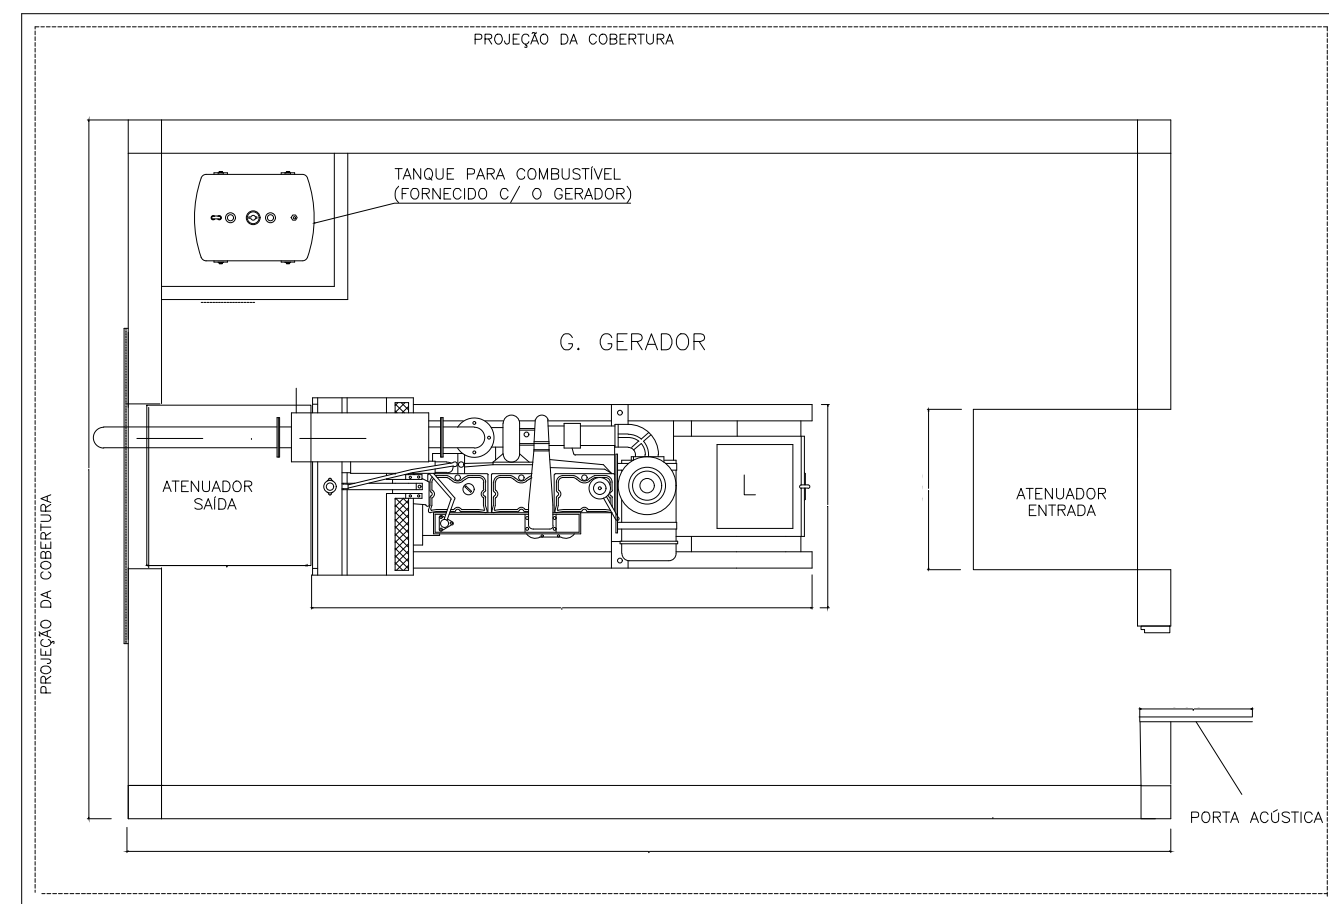


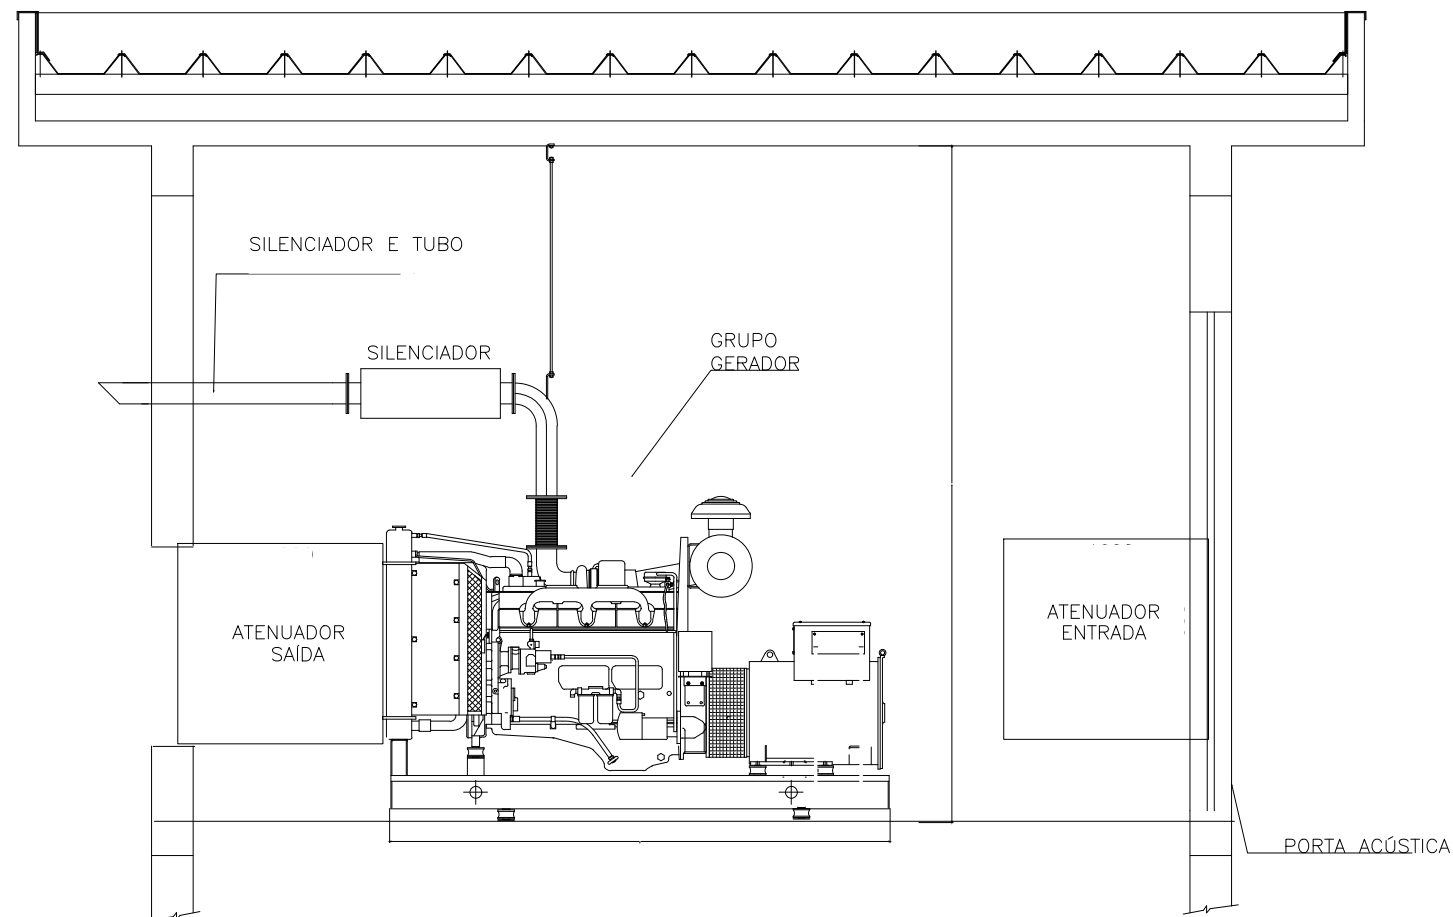

OBSERVAÇÕES

- 1 - MEDIDAS EM MILÍMETROS
- 2 - AS MEDIDAS INDICAM AS DIMENSÕES SUGERIDAS PARA SALA DO GRUPO DIESEL GERADOR
- 3 - ACEITAVEL VARIAÇÃO DE ATÉ $\pm 10\%$

LAYOUT SUGESTIVO

T.E.	DATA	DESCRIÇÃO	PROJ.	DES.	VER.	APR.	T.E.(TIPO DE EMISSÃO)		VISTO E ACEITO ESTA ACEITAÇÃO NÃO ISENTA A CONTRATADA DAS RESPONSABILIDADES E OBRIGAÇÕES ESTABELECIDAS NO CONTRATO		 RUA CEL. FIGUEIREDO, 238 - BH/MG (31) 3424-1881 RESPONSÁVEL TÉCNICO MÁRIO SÉRGIO TURRA LIAL CREA-SP 127064/D	DIMENSIONAL SALA PARA GRUPO DIESEL GERADOR ABERTO COM KIT ATENUAÇÃO		N°. MS:			
		CONFORME CONSTRUÍDO	MST	JMZ	MST	MST	(A) PRELIMINAR (B) PARA APROVAÇÃO (C) PARA CONHECIMENTO (D) PARA COTAÇÃO	(E) PARA CONSTRUÇÃO (F) CONFORME COMPRADO (G) CONFORME CONSTRUÍDO (H) CANCELADO	ANALISADO:			CONTEÚDO GRUPO DIESEL GERADOR	FORMATO: A4	FOLHA:	N° CONTRATADA:	ESCALA: SEM ESCALA	