
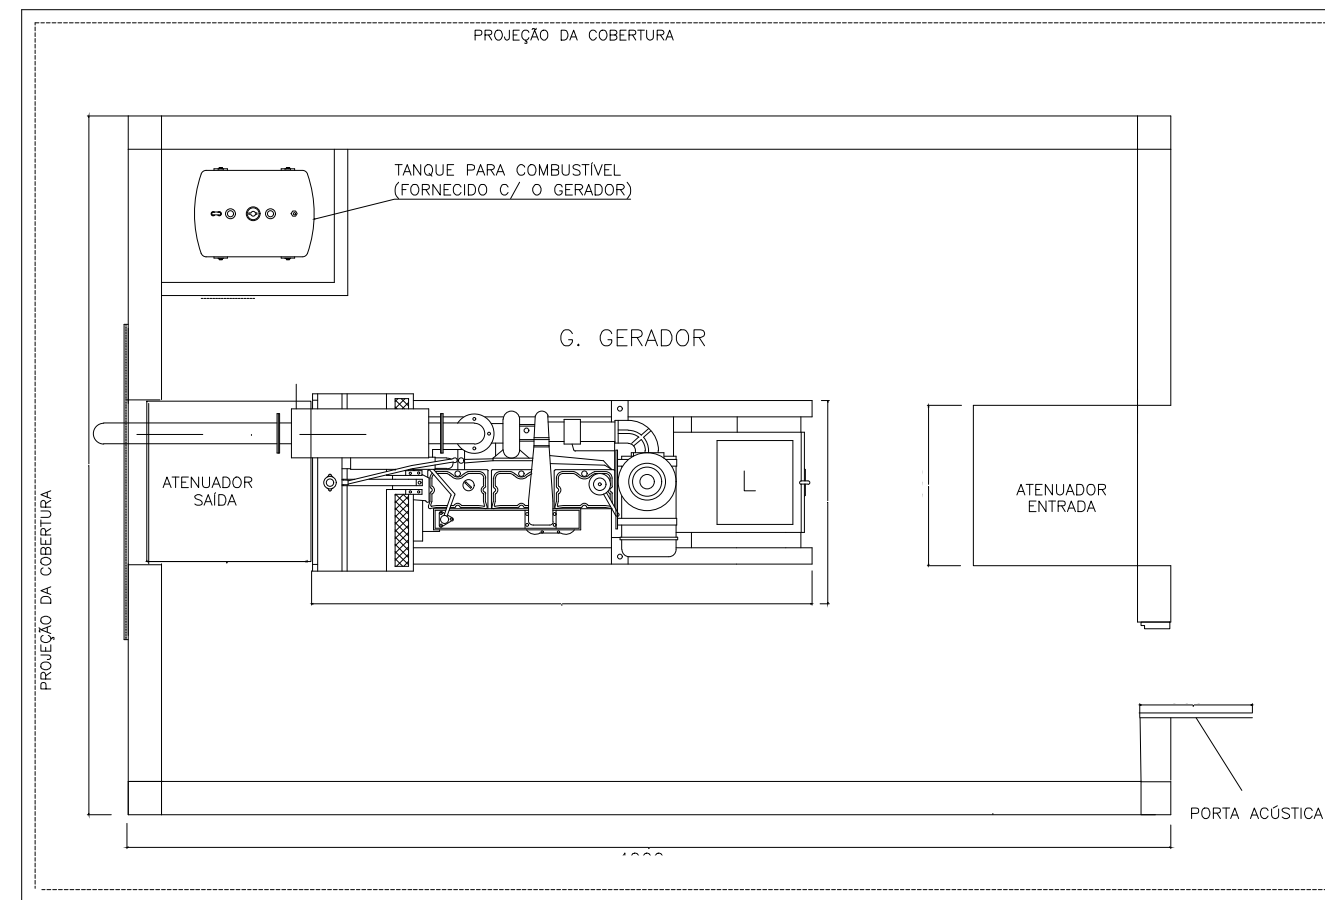


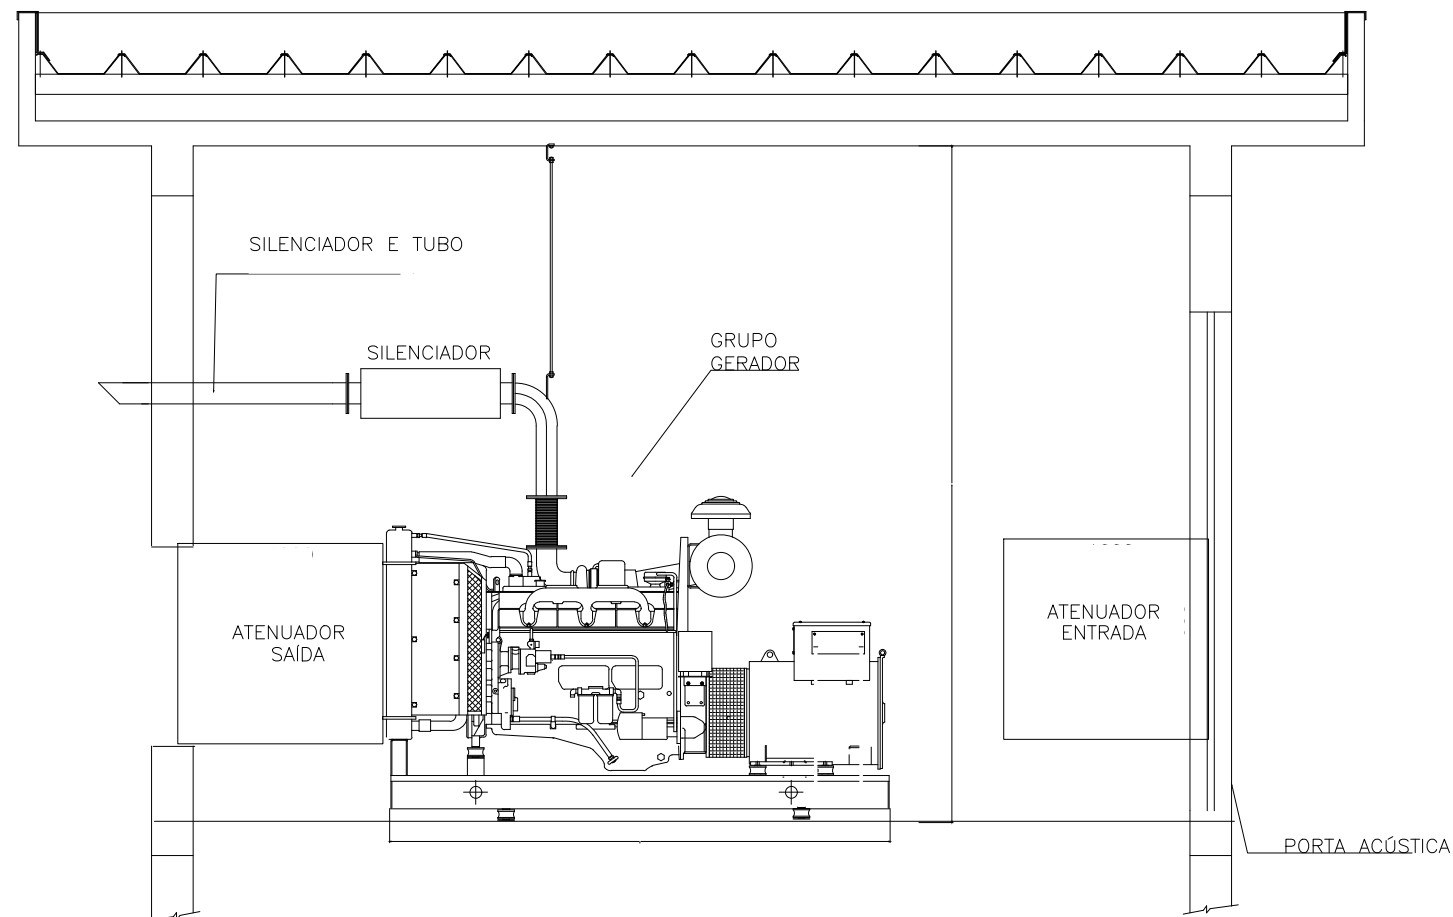

OBSERVAÇÕES

- 1 - MEDIDAS EM MILÍMETROS
- 2 - AS MEDIDAS INDICAM AS DIMENSÕES SUGERIDAS PARA SALA DO GRUPO DIESEL GERADOR
- 3 - ACEITAVEL VARIAÇÃO DE ATÉ ± 10%

LAYOUT SUGESTIVO

| T.E. | DATA | DESCRIÇÃO           | PROJ. | DES. | VER. | APR. | T.E.(TIPO DE EMISSÃO) |                         | VISTO E ACEITO<br>ESTA ACEITAÇÃO NÃO ISENTA A CONTRATADA DAS RESPONSABILIDADES E OBRIGAÇÕES ESTABELECIDAS NO CONTRATO | <br>RUA CEL. FIGUEIREDO, 238 - BH/MG<br>(31) 3424-1881<br>RESPONSÁVEL TÉCNICO<br>MÁRIO SÉRGIO TURRA LIAL<br>CREA-SP 127064/D | DIMENSIONAL SALA PARA GRUPO DIESEL GERADOR ABERTO COM KIT ATENUAÇÃO |  | Nº. MS:         |            |
|------|------|---------------------|-------|------|------|------|-----------------------|-------------------------|---|---|---------------------------------------------------------------------|--|-----------------|------------|
|      |      | CONFORME CONSTRUÍDO | MST   | JMZ  | MST  | MST  | (A) PRELIMINAR        | (E) PARA CONSTRUÇÃO     |   |   | CONTEÚDO<br>GRUPO DIESEL GERADOR                                    |  | FORMATO:        | FOLHA:     |
|      |      |                     |       |      |      |      | (B) PARA APROVAÇÃO    | (F) CONFORME COMPRADO   |   |   |                                                                     |  | A4              |            |
|      |      |                     |       |      |      |      | (C) PARA CONHECIMENTO | (G) CONFORME CONSTRUÍDO |   |   |                                                                     |  | Nº. CONTRATADA: |            |
|      |      |                     |       |      |      |      | (D) PARA COTAÇÃO      | (H) CANCELADO           |   |   |                                                                     |  | ESCALA:         | SEM ESCALA |