
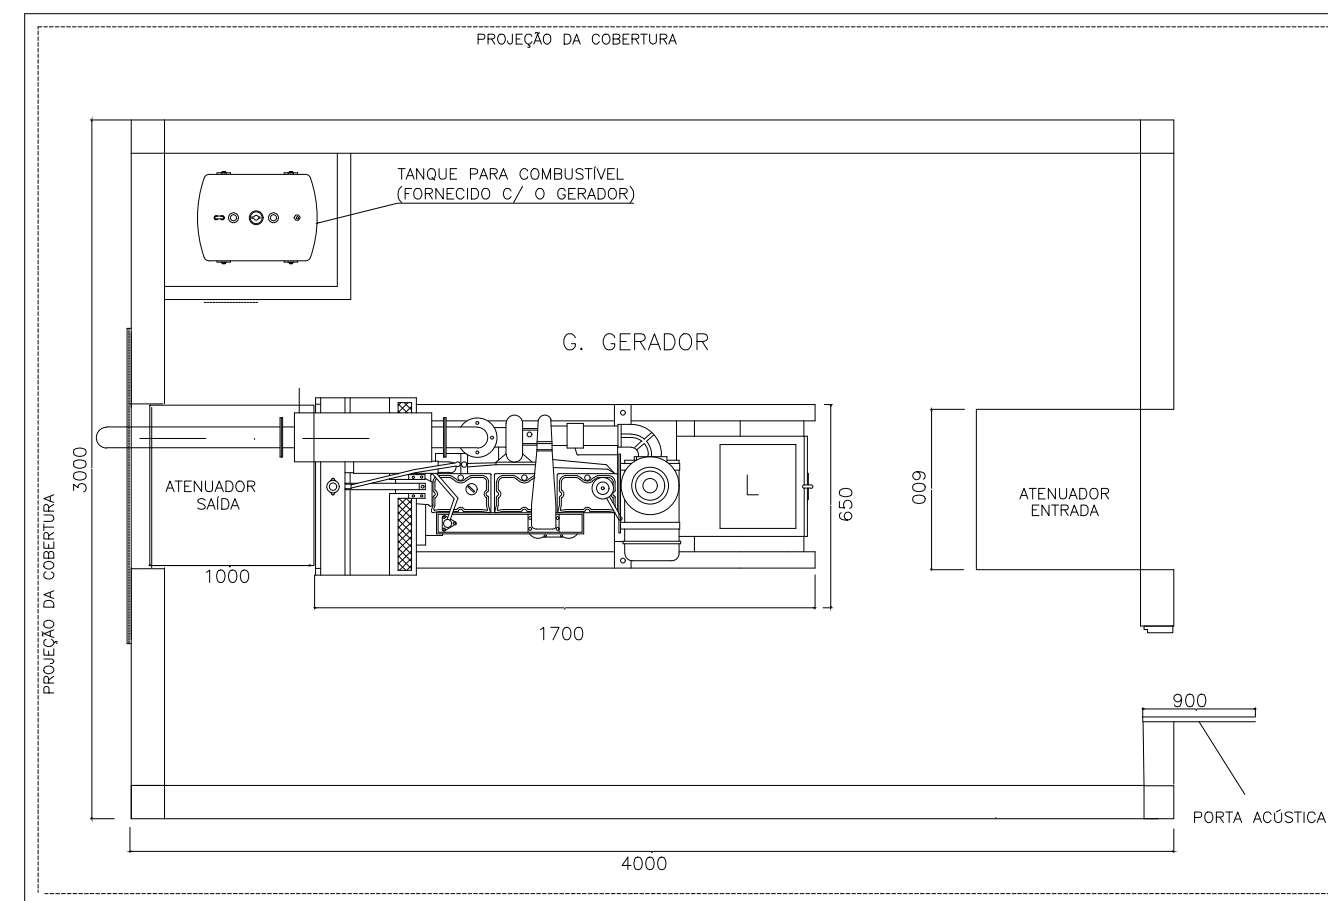


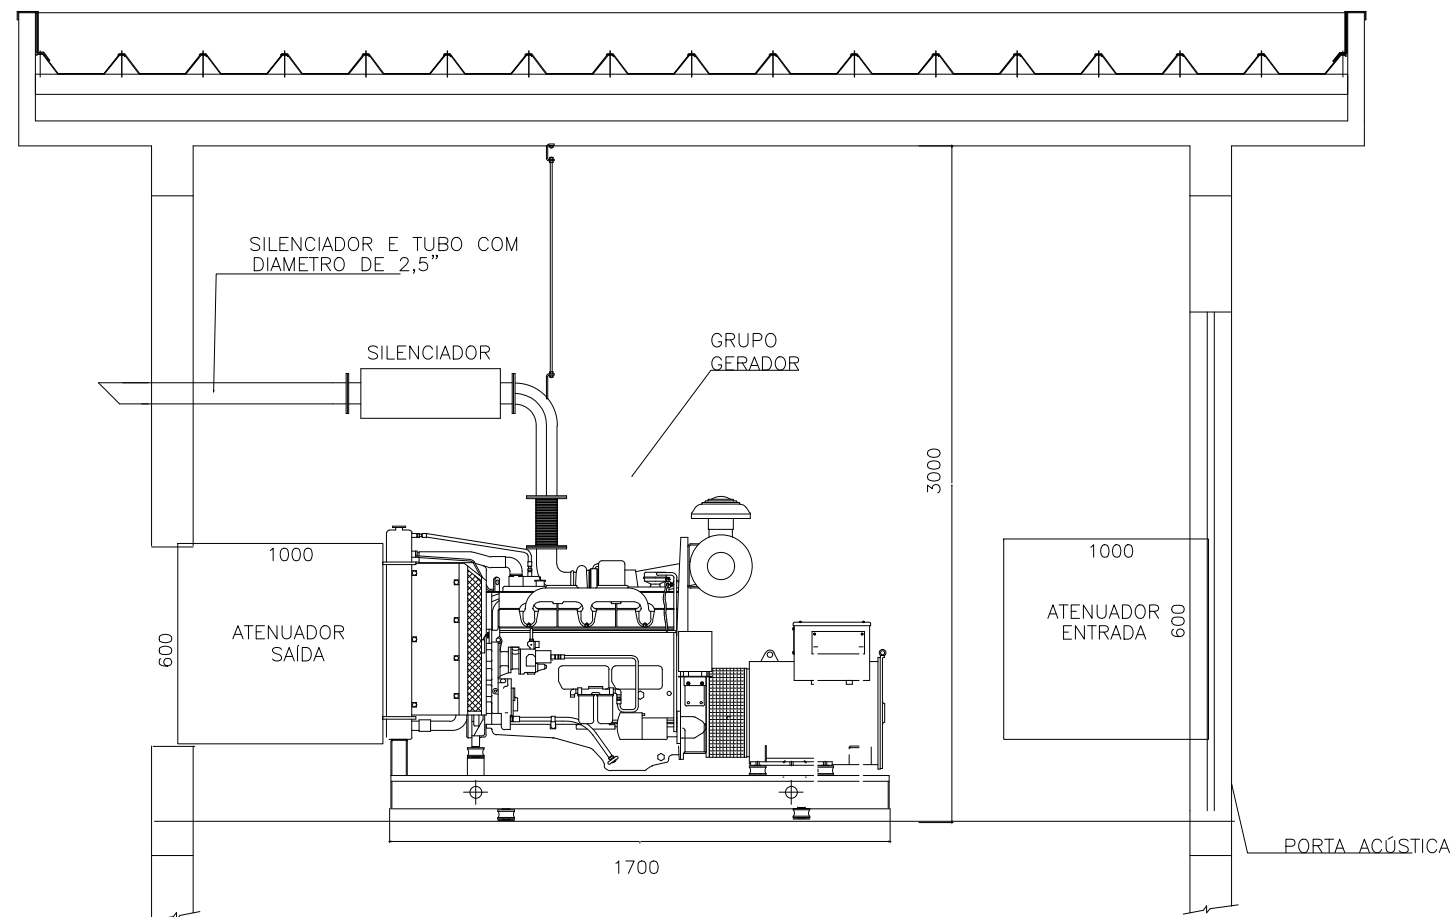

OBSERVAÇÕES

- 1 - MEDIDAS EM MILÍMETROS
- 2 - AS MEDIDAS INDICAM AS DIMENSÕES SUGERIDAS PARA SALA DO GRUPO DIESEL GERADOR
- 3 - ACEITAVEL VARIAÇÃO DE ATÉ $\pm 10\%$

LAYOUT SUGESTIVO

T.E.	DATA	DESCRIÇÃO	PROJ.	DES.	VER.	APR.	T.E.(TIPO DE EMISSÃO)	VISTO E ACEITO ESTA ACEITAÇÃO NÃO ISENTA A CONTRATADA DAS RESPONSABILIDADES E OBRIGAÇÕES ESTABELECIDAS NO CONTRATO		 RUA CEL. FIGUEIREDO, 238 - BH/MG (31) 3424-1881 RESPONSÁVEL TÉCNICO MÁRIO SÉRGIO TURRA LIAL CREA-SP 127064/D	DIMENSIONAL SALA PARA GRUPO DIESEL GERADOR ABERTO COM KIT ATENUAÇÃO	Nº. MS:	
		CONFORME CONSTRUÍDO	MST	JMZ	MST	MST	(A) PRELIMINAR (B) PARA APROVAÇÃO (C) PARA CONHECIMENTO (D) PARA COTAÇÃO (E) PARA CONSTRUÇÃO (F) CONFORME COMPRADO (G) CONFORME CONSTRUÍDO (H) CANCELADO				CONTEÚDO GRUPO DIESEL GERADOR	FORMATO: A4	FOLHA:
								ANALISADO:				Nº. CONTRATADA:	
								ACEITO:				ESCALA: SEM ESCALA	
								VISTO:					